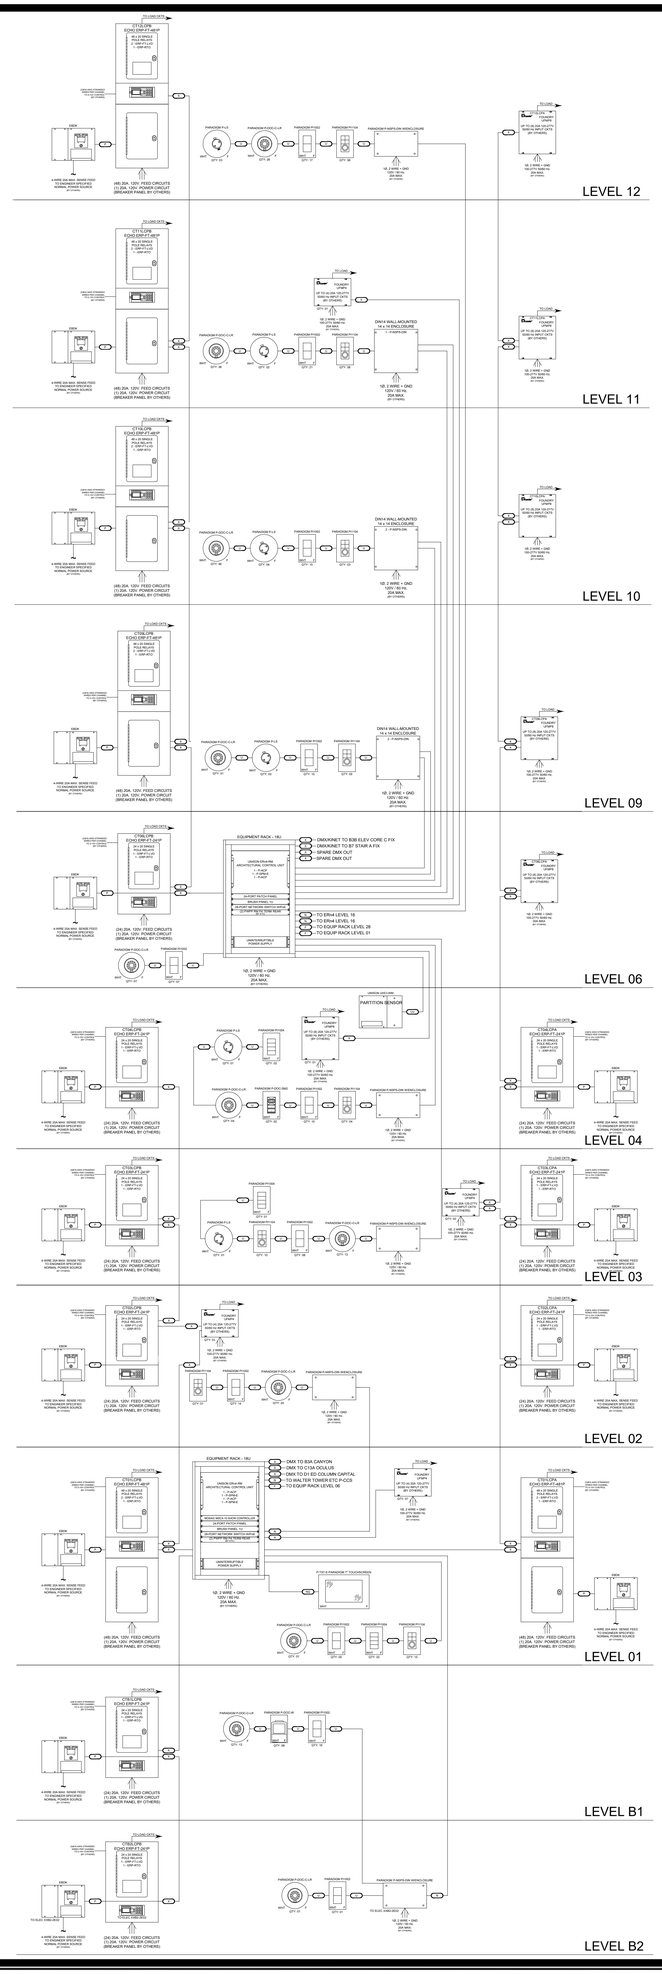


CONTROL WIRING LEGEND

SYMBOL	WIRE TYPE(S)	SIGNAL
DC	(1) BELDEN #9729	DMX OUTPUT
NC	(1) BELDEN #1583A	ETCNet (Cat5e)
NCG	(1) BELDEN #1583A (1) #14 AWG. STRANDED GND WIRE	ETCNet WITH GROUND (Cat5e)
UP	(1) BELDEN #8471 (1) #14 AWG. STRANDED GND WIRE	UNISON
FO	(1) BELDEN #FI3D000R9	FIBER
BP	(2) #16 AWG. STRANDED WIRES	PANIC

* = WIRE IDENTIFICATION NUMBER (NOT QUANTITY)

NOTES:

1.) ALL CONTROL WIRING IS PROVIDED BY OTHERS UNLESS NOTED OTHERWISE.

2.) ALL ETCNet RUNS SHALL BE CONTINUOUS, UNSPLICED RUNS LESS THAN 300 FEET (90 METERS). ALL NETWORK CONNECTIONS TO BE TIA/EIA 568B.

ETC, Inc.

3031 Pleasant View Rd
PO Box 620979
Middleton WI 53562-0979
Tel +1 608 831 4116
Toll Free +1 800 688 4116
Fax +1 608 836 1736
etcconnect.com

UNLESS OTHERWISE SPECIFIED ALL DIMENSIONS ARE IN INCHES.

ORIGINAL FILE:
TITLE.DWG

CONTRACT WITH:
CED - HOUSTON

REPRESENTATIVE:
CW LIGHTING

PROJECT MANAGER:
AARON BERTSCH

APPLICATIONS ENGINEER:
BILL KUNDE

DRAWING TITLE:
RISER


AB	**7/23/26**	**F**
AB	9/2e6/24	C
AB	8/16/24	B
AB	7/18/24	A
AB	3/4/24	SUBMITTAL
BY	DATE	REV.

JOB:
Houston Methodist Centennial Hospital

LOCATION:
Houston, TX

JOB NUMBER:
15076538

DRAWING:
001

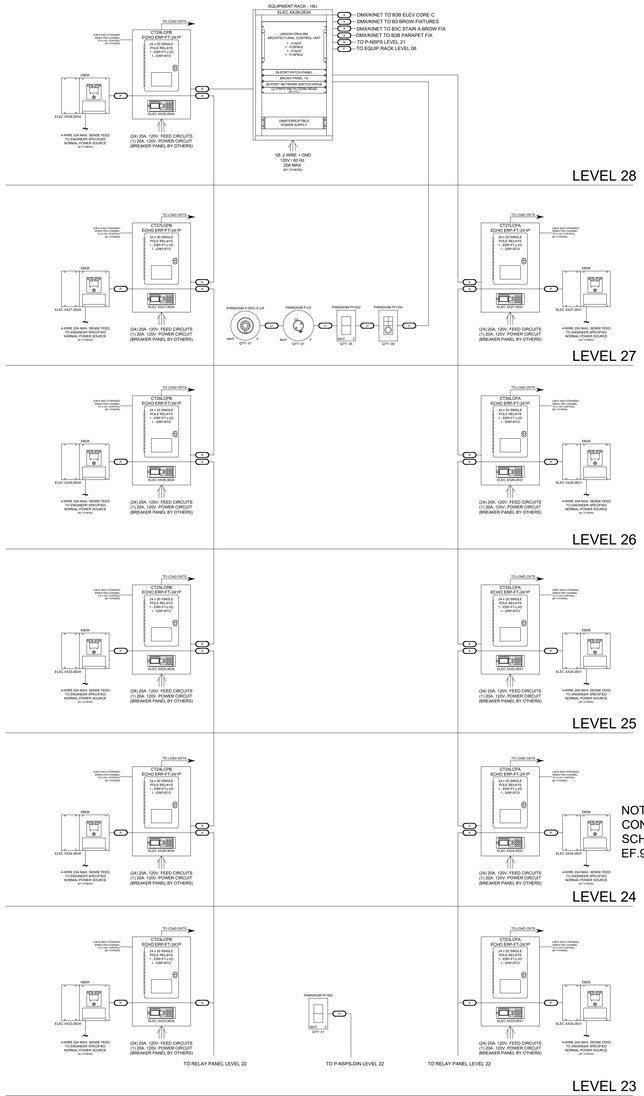

CONTROL WIRING LEGEND

SYMBOL	WIRE TYPE(S)	SIGNAL
XC	(1) BELDEN #9729	DMX OUTPUT
NC	(1) BELDEN #1583A	ETCNet (Cat5e)
NCG	(1) BELDEN #1583A (1) #14 AWG. STRANDED GND WIRE	ETCNet WITH GROUND (Cat5e)
UT	(1) BELDEN #8471 (1) #14 AWG. STRANDED GND WIRE	UNISON
FC	(1) BELDEN #FI3D006FRI	FIBER
PT	(2) #16 AWG. STRANDED WIRES	PANIC

* = WIRE IDENTIFICATION NUMBER (NOT QUANTITY)

NOTES:

1.) ALL CONTROL WIRING IS PROVIDED BY OTHERS UNLESS NOTED OTHERWISE.

2.) ALL ETCNet RUNS SHALL BE CONTINUOUS. UNSPLICED RUNS LESS THAN 300 FEET (90 METERS). ALL NETWORK CONNECTIONS TO BE TIA/EIA 568B.

ETC, Inc.

3031 Pleasant View Rd
PO Box 620979
Middleton WI 53562-0979
Tel +1 608 831 4116
Toll Free +1 800 688 4116
Fax +1 608 836 1736
etcconnect.com

UNLESS OTHERWISE SPECIFIED ALL DIMENSIONS ARE IN INCHES.

ORIGINAL FILE:
TITLE.DWG

CONTRACT WITH:
CED - HOUSTON

REPRESENTATIVE:
CW LIGHTING

PROJECT MANAGER:
AARON BERTSCH

APPLICATIONS ENGINEER:
BILL KUNDE

DRAWING TITLE:
RISER

AB	**7/23/26**	**F**
AB	9/26/24	C
AB	8/16/24	B
AB	7/18/24	A
AB	3/4/24	SUBMITTAL
BY	DATE	REV.

JOB:
Houston Methodist Centennial Hospital

LOCATION:
Houston, TX

JOB NUMBER:
15076538

DRAWING:
002